


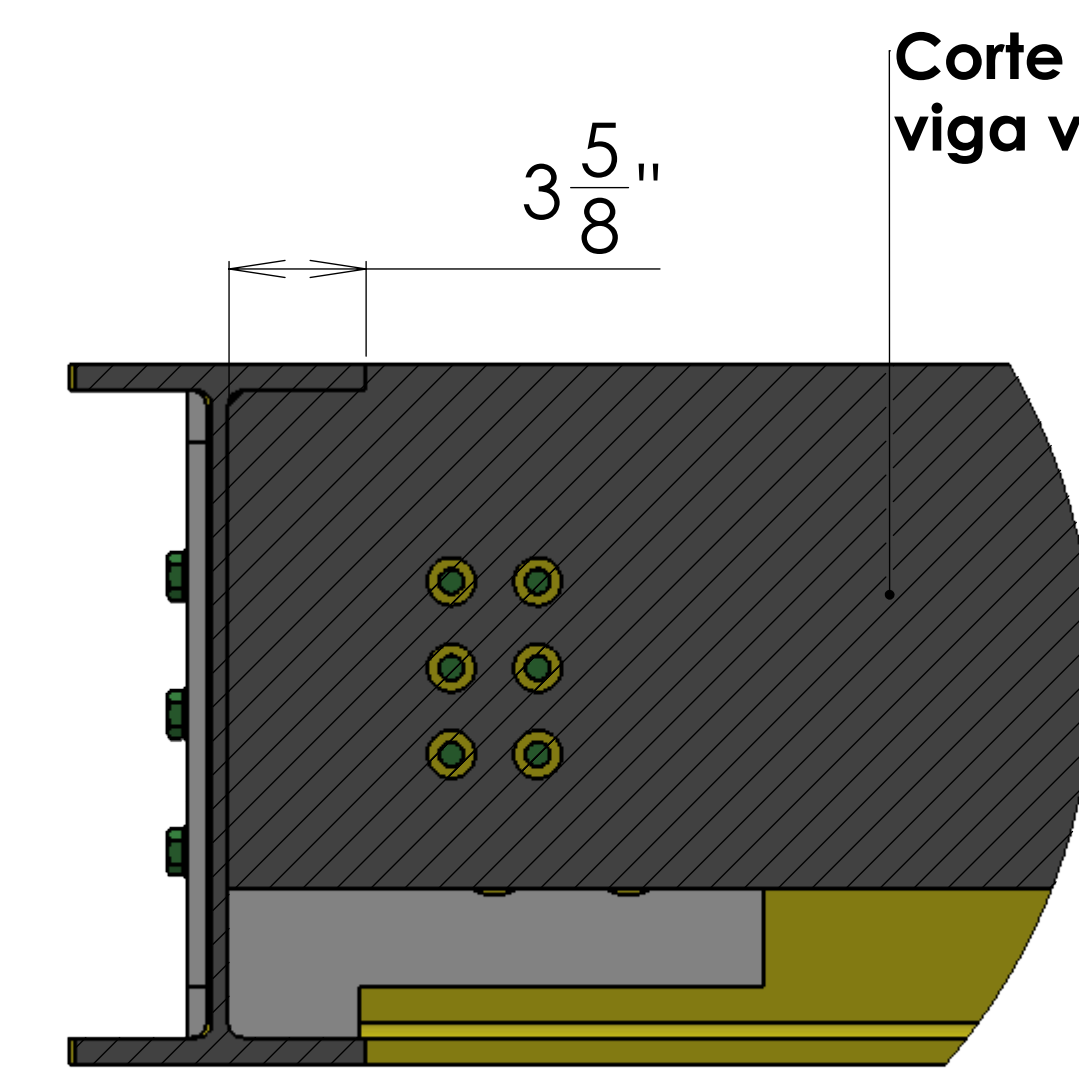


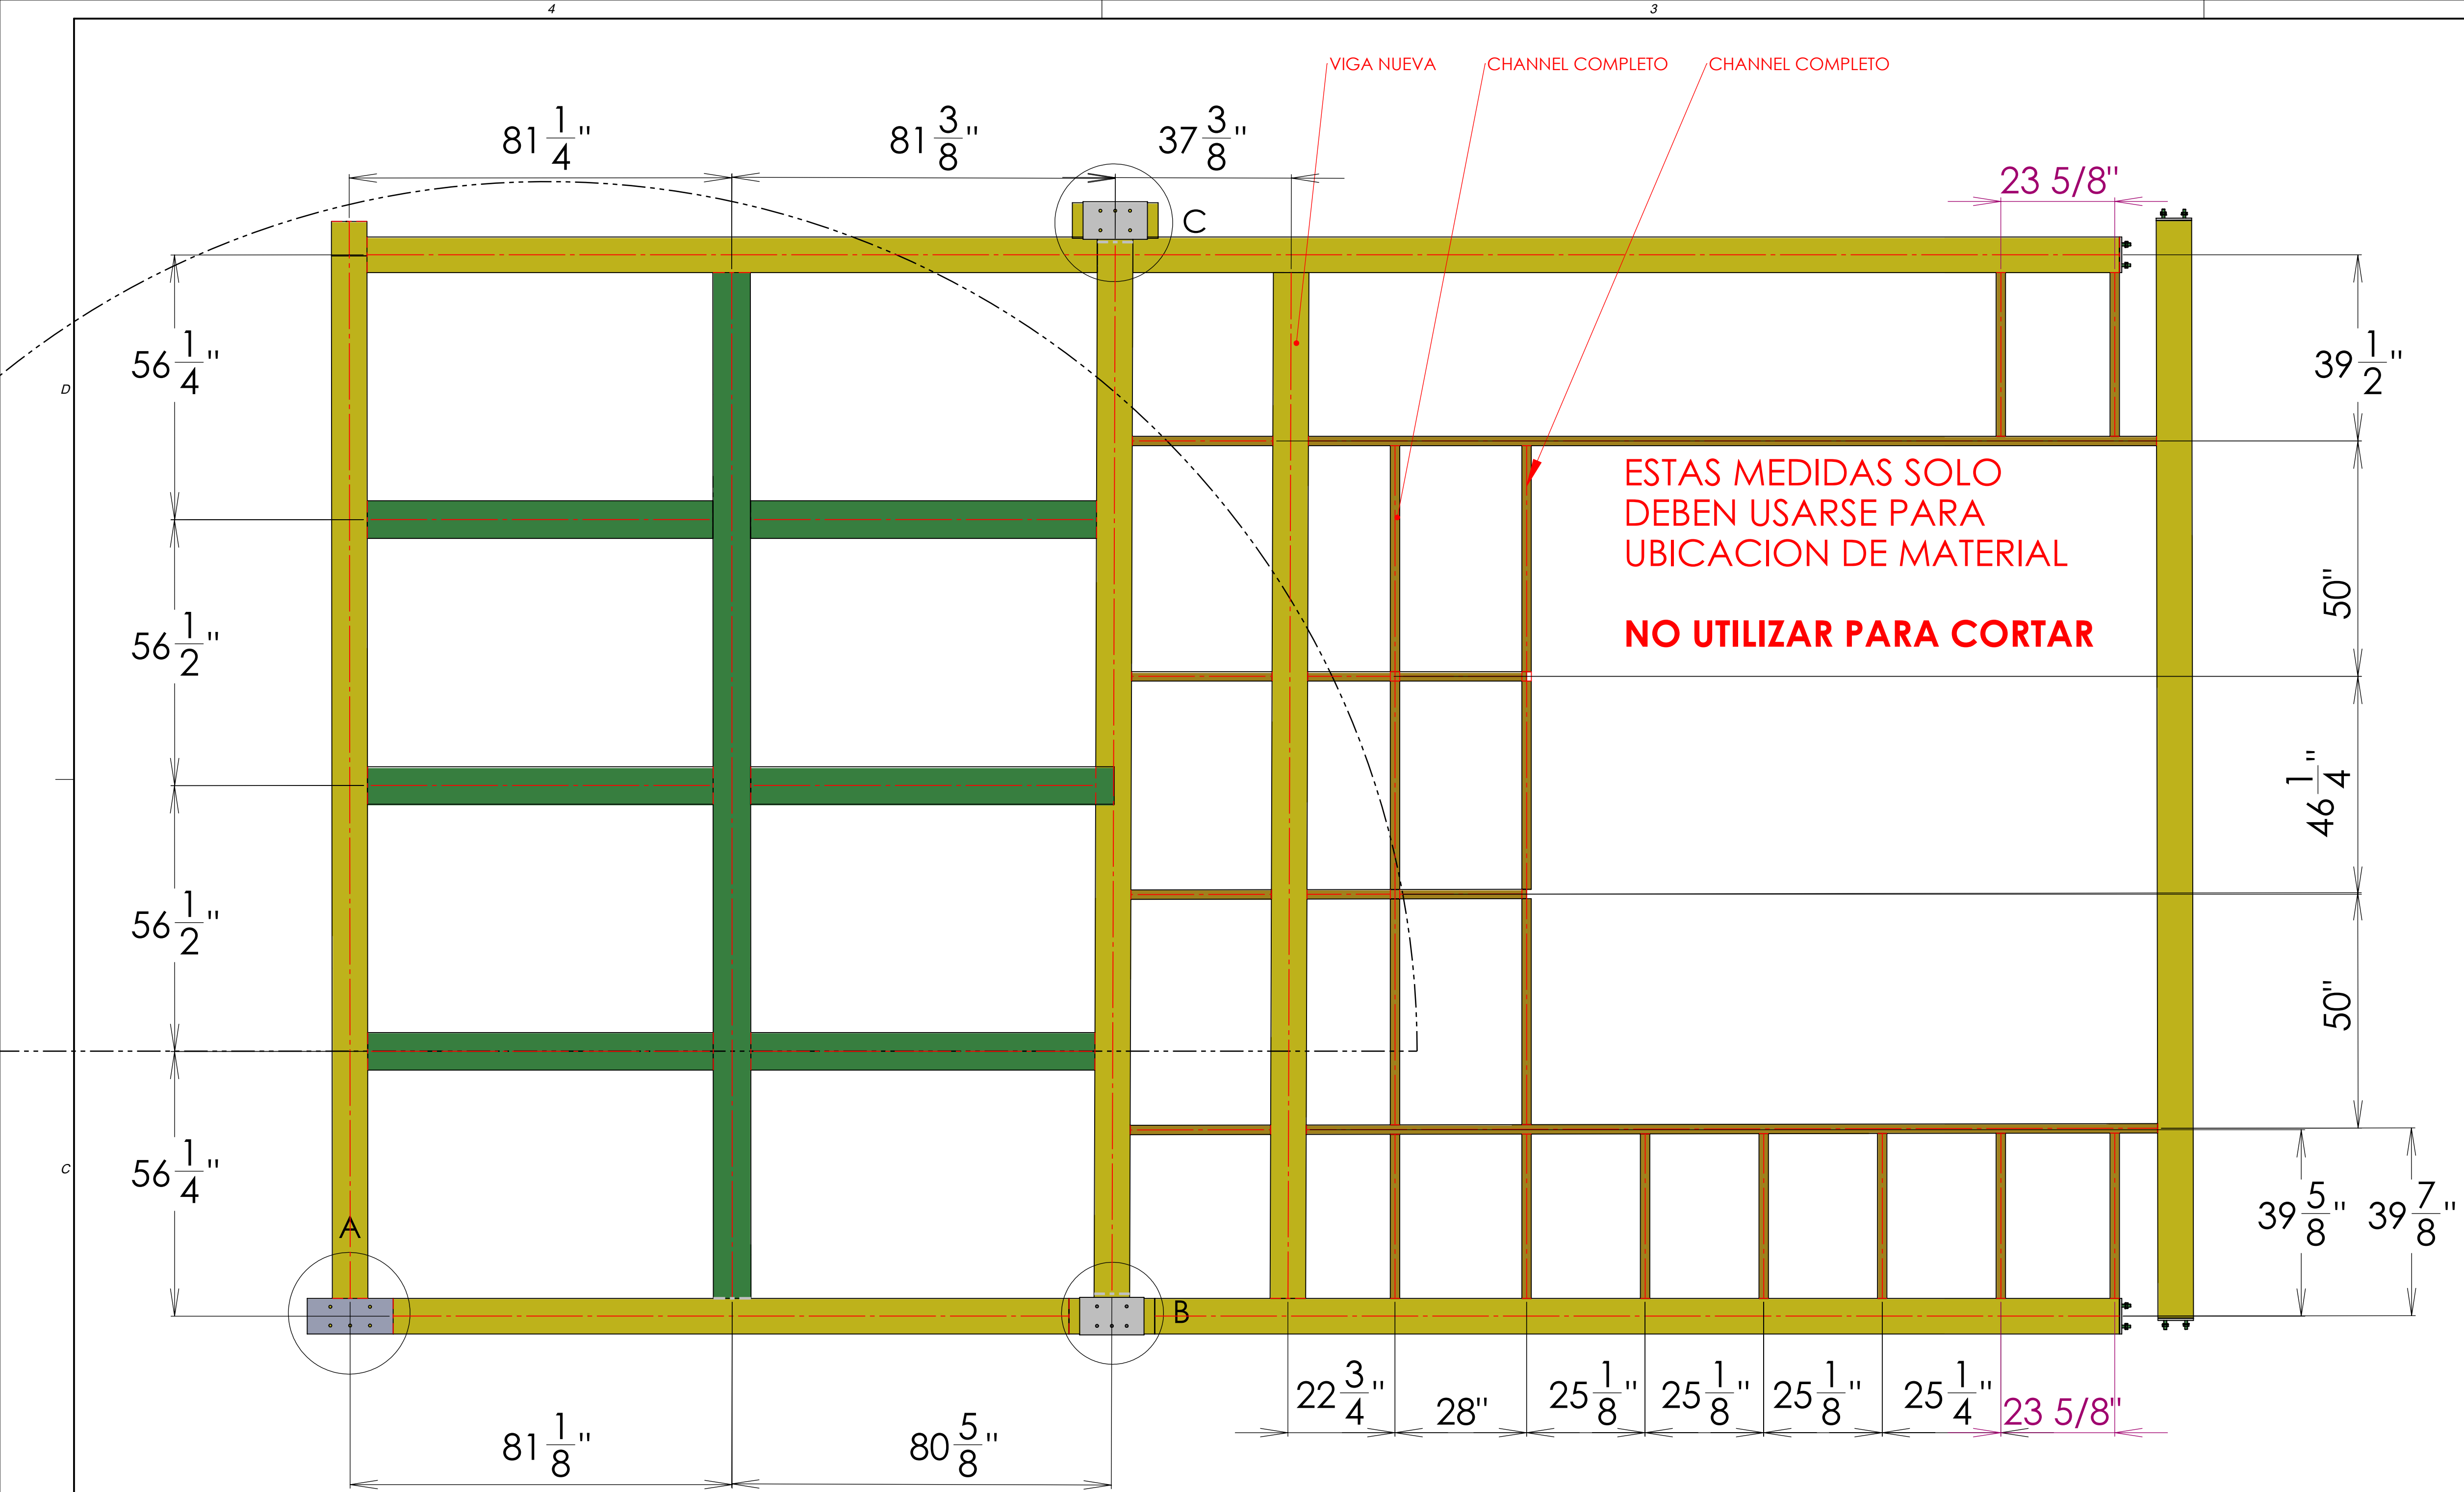

DETALLE I
ESCALA 1:5

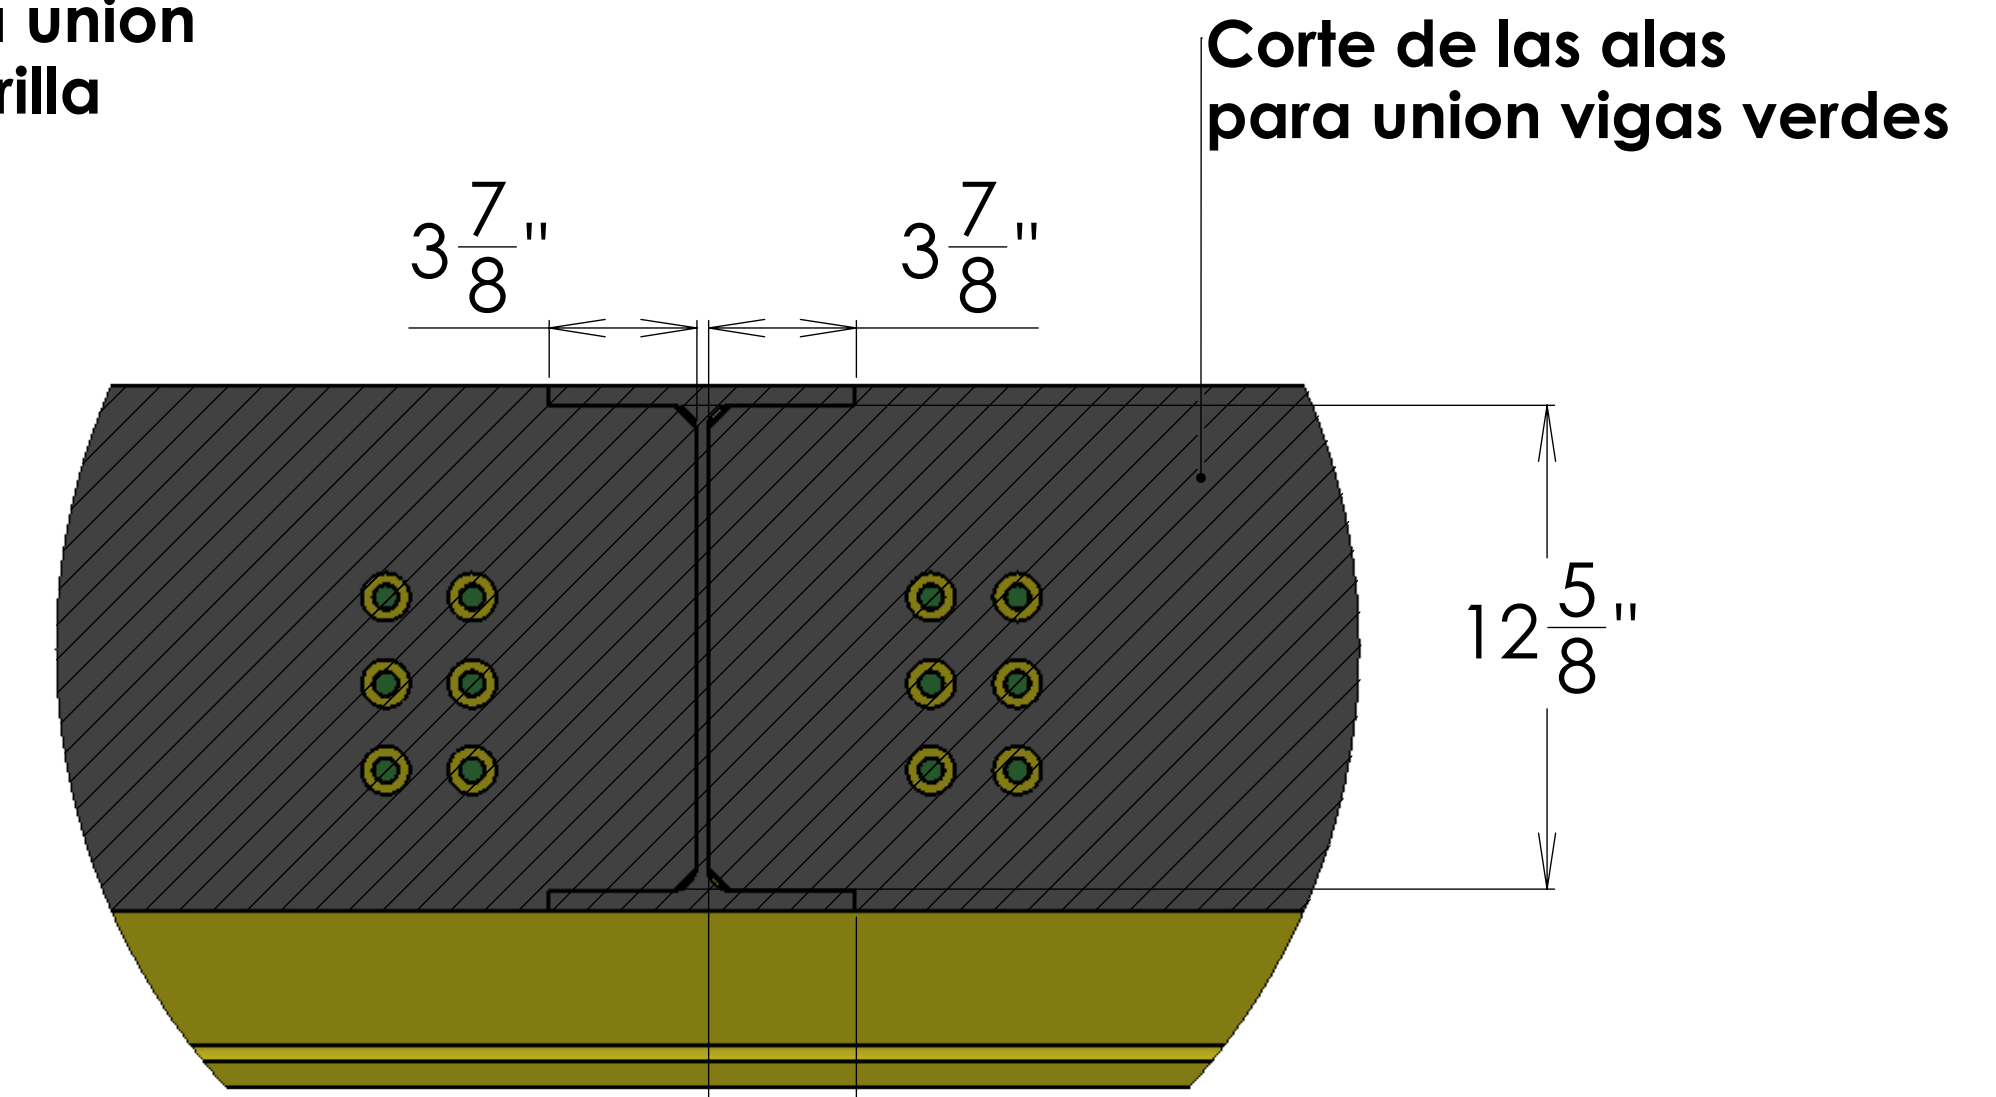


DETALLE K
ESCALA 1:5


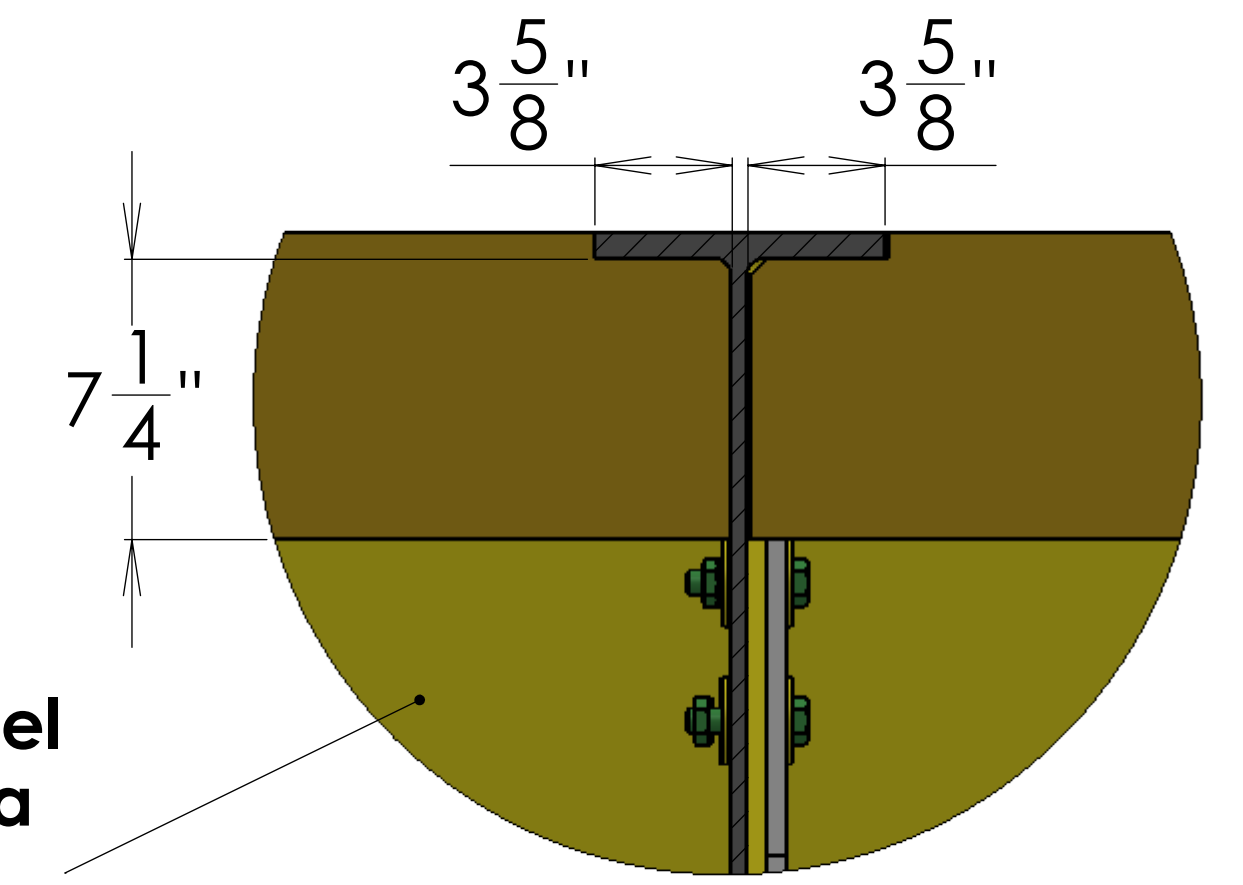


DETALLE L
ESCALA 1:5


Corte de channel
para entrar en la
viga naranja

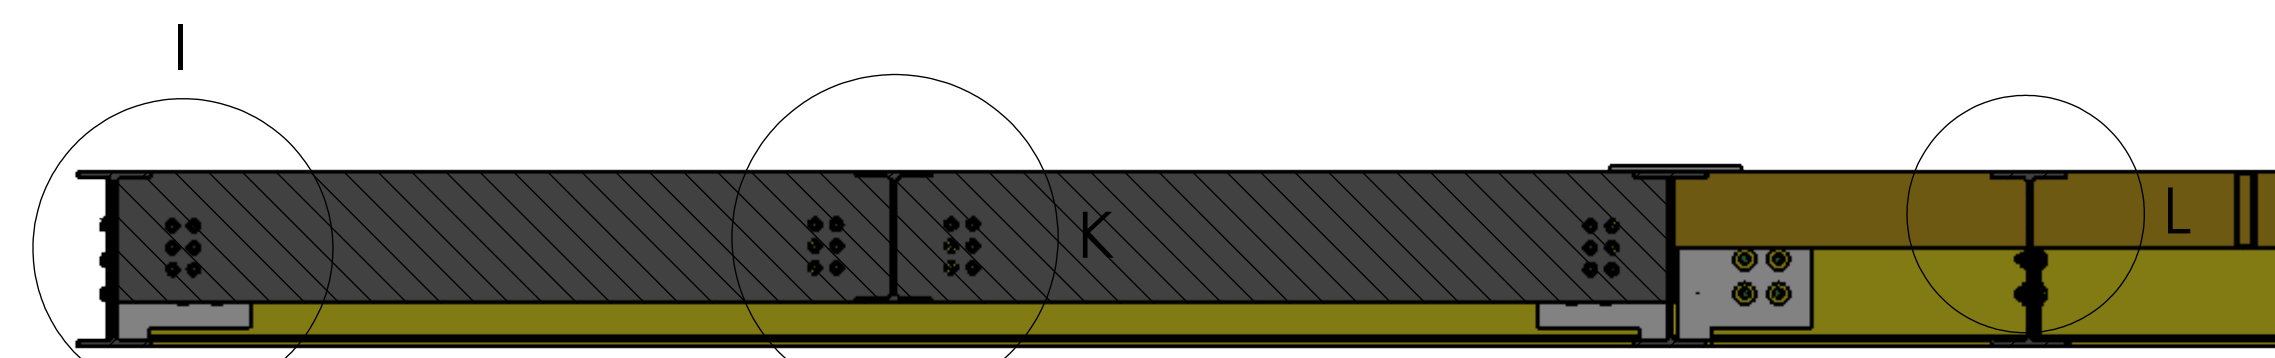


SECCIÓN H-H

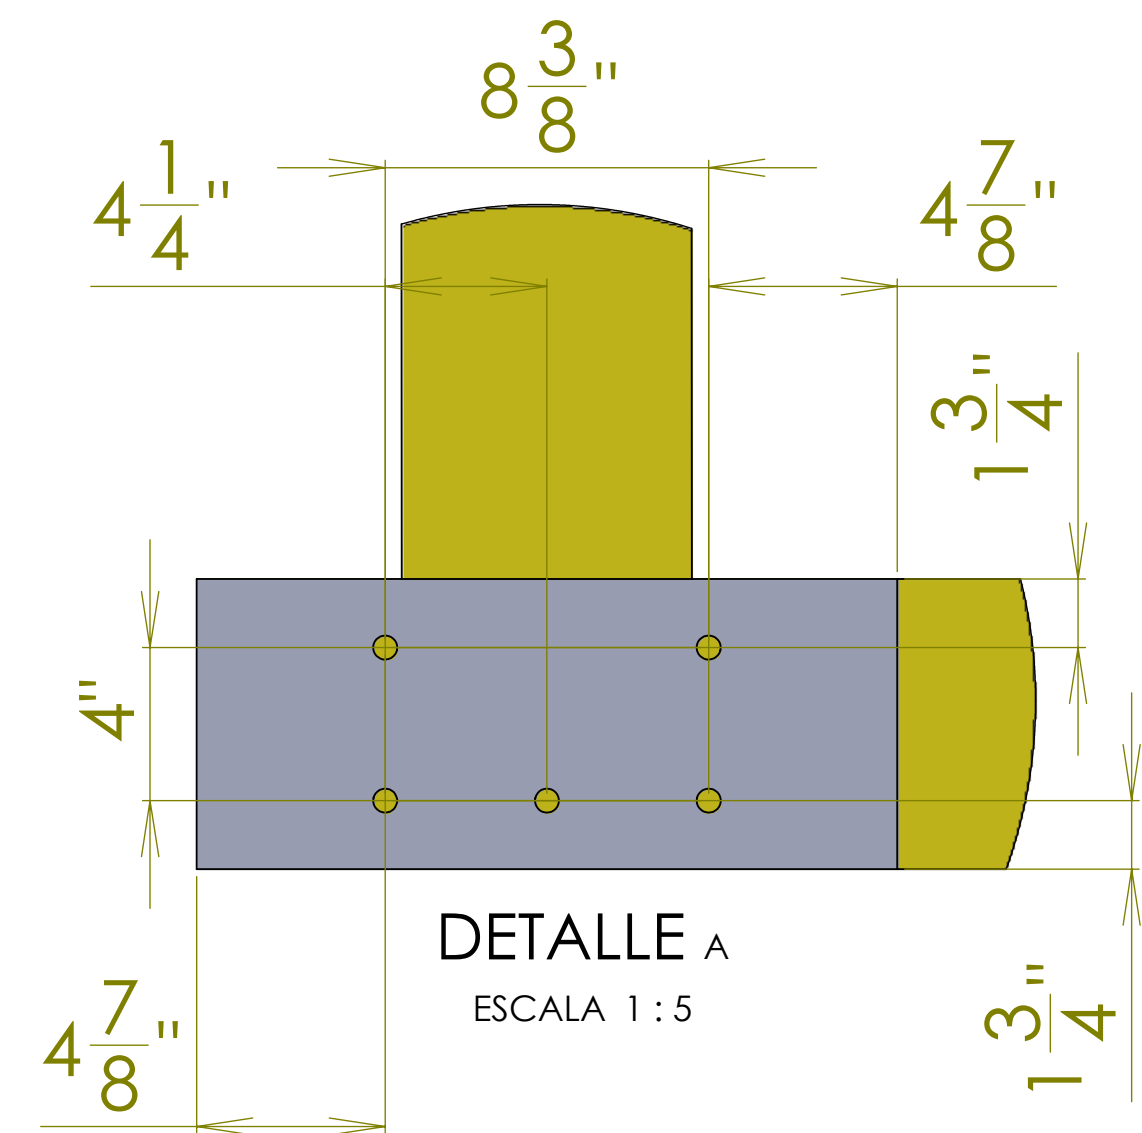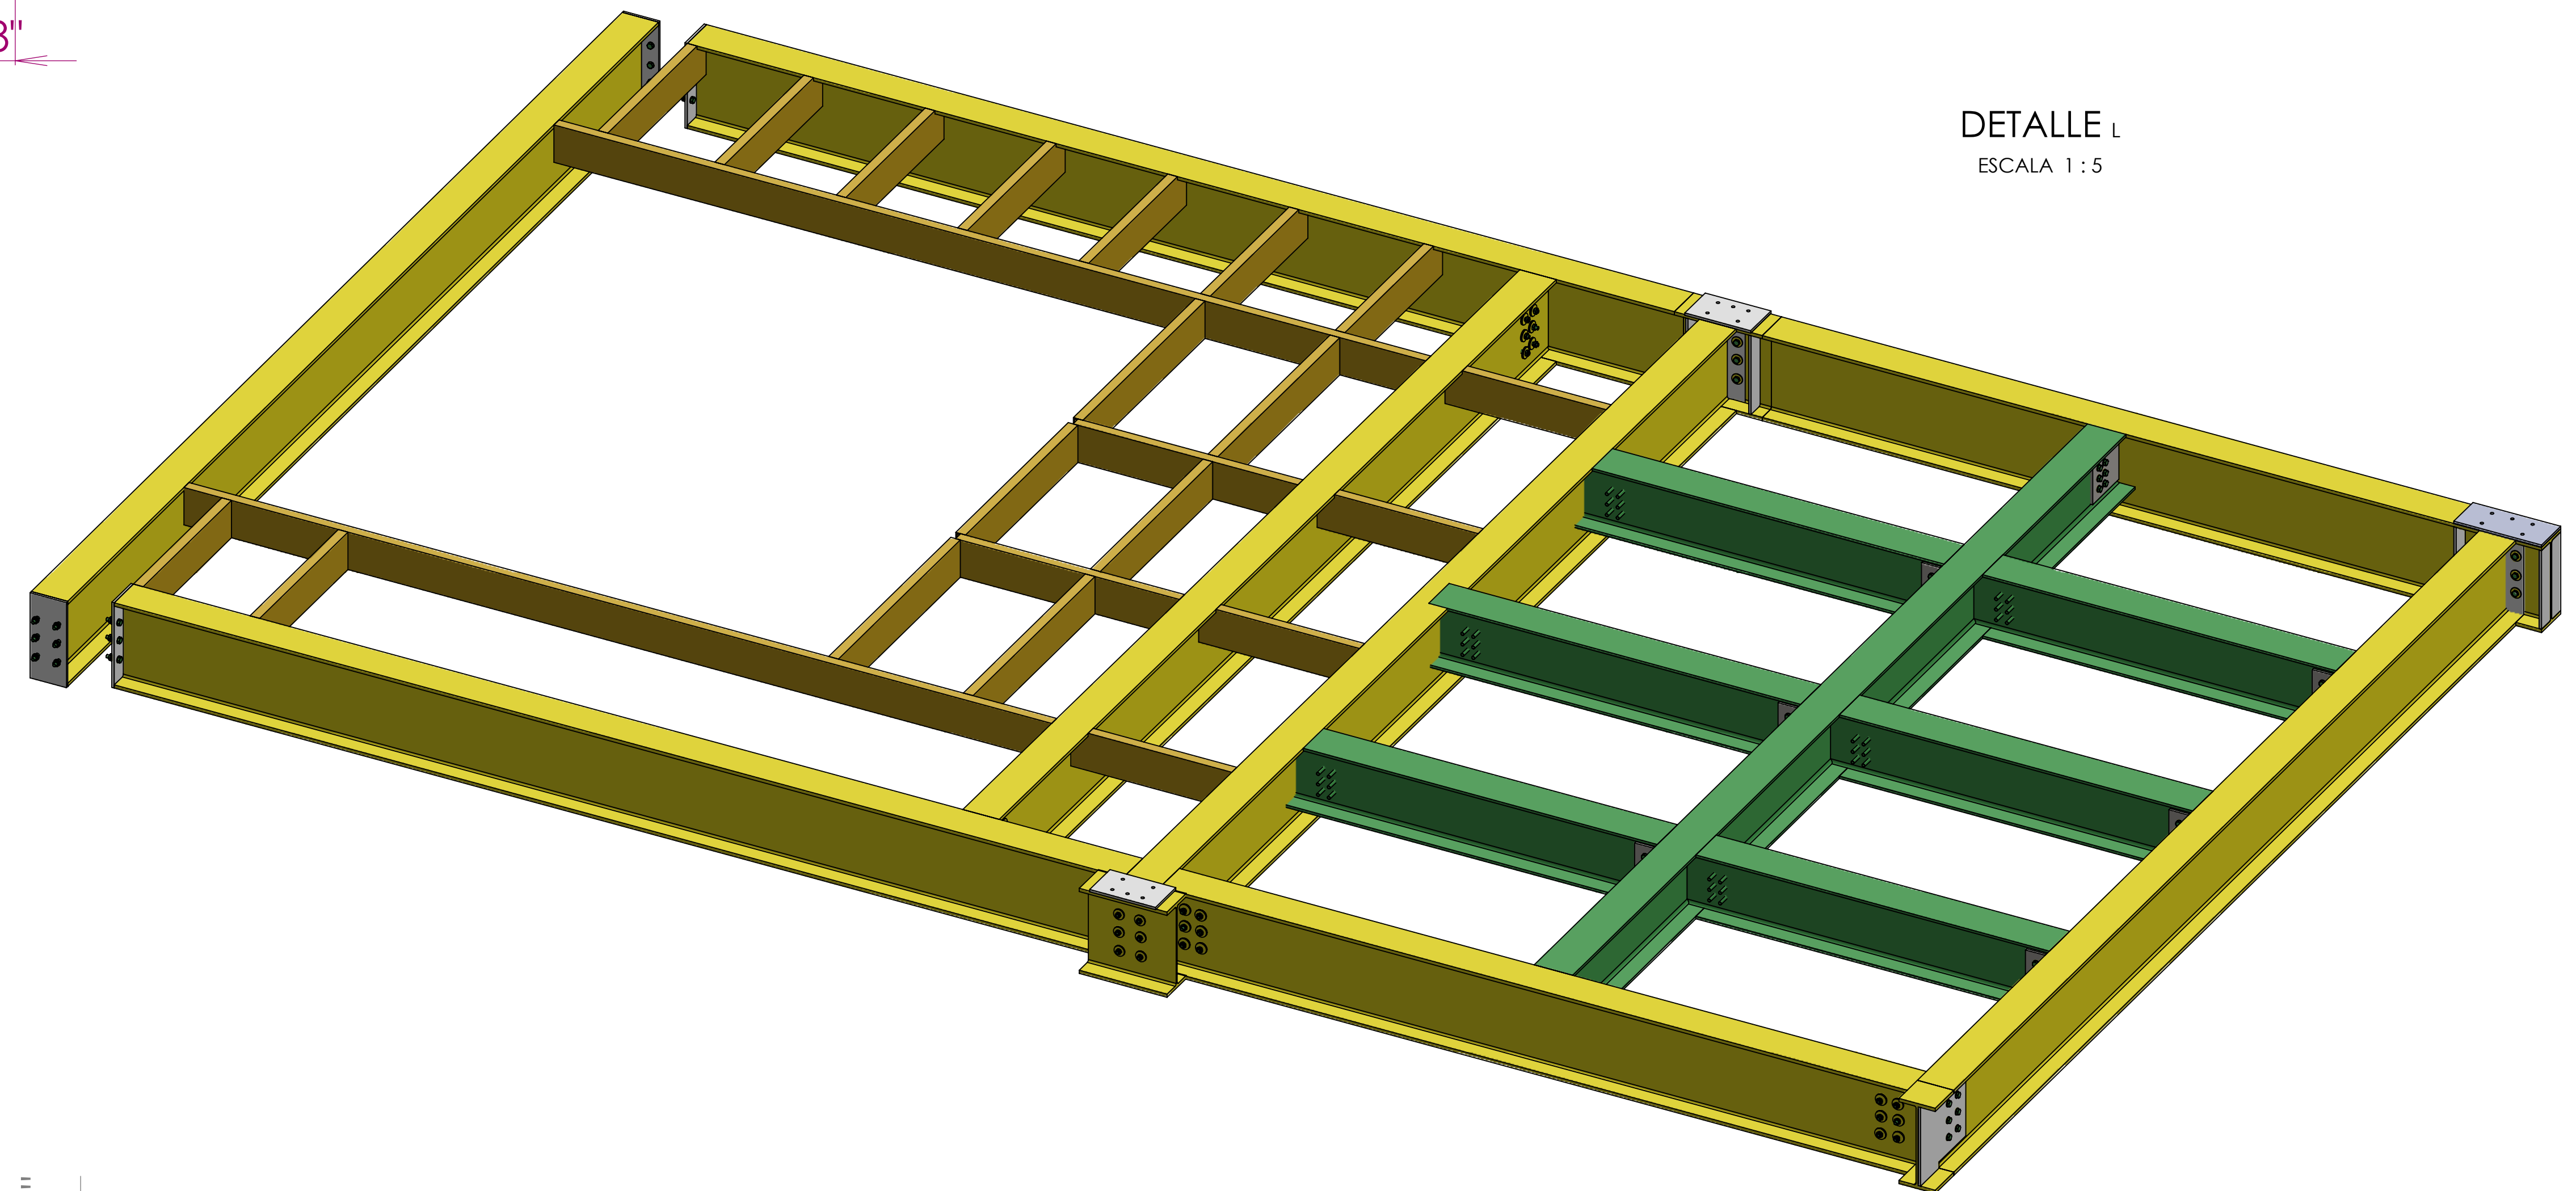

DETALLE A
ESCALA 1:5

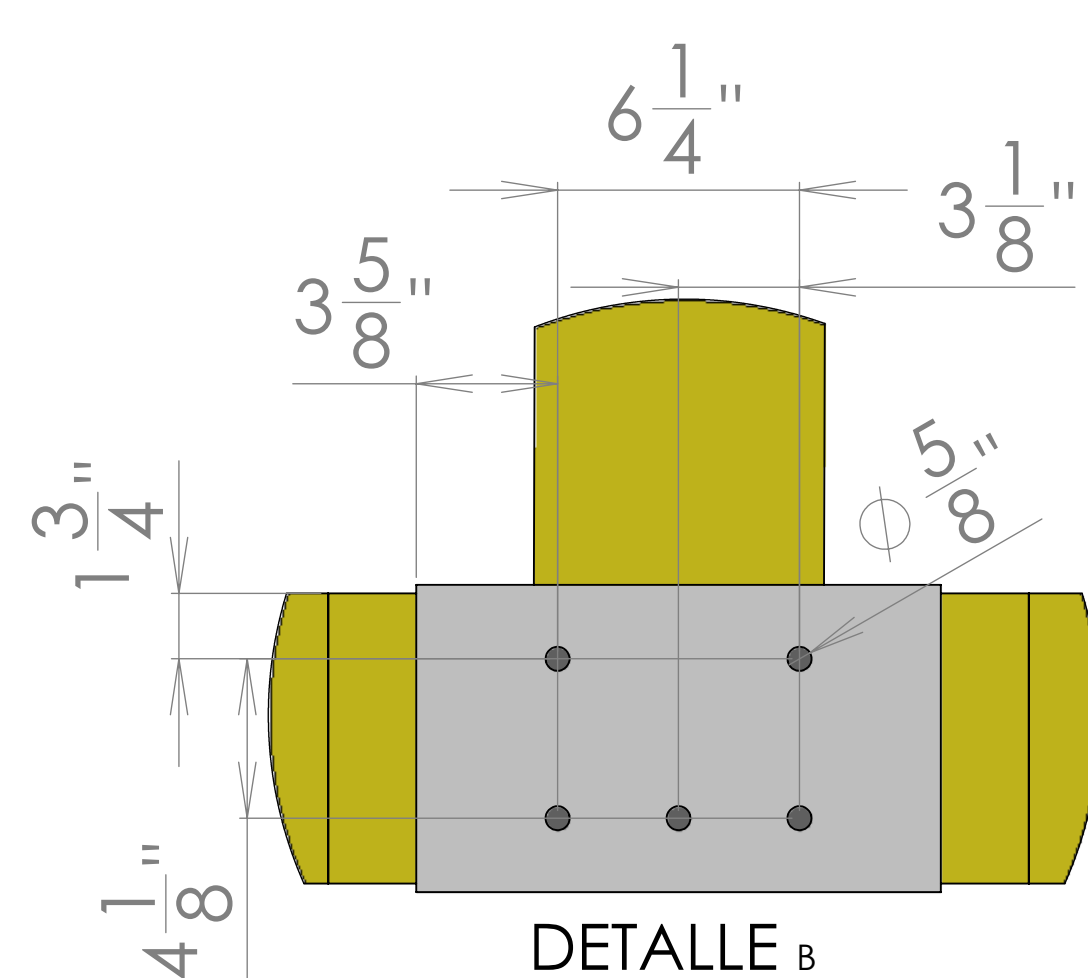

DETALLE B
ESCALA 1:5

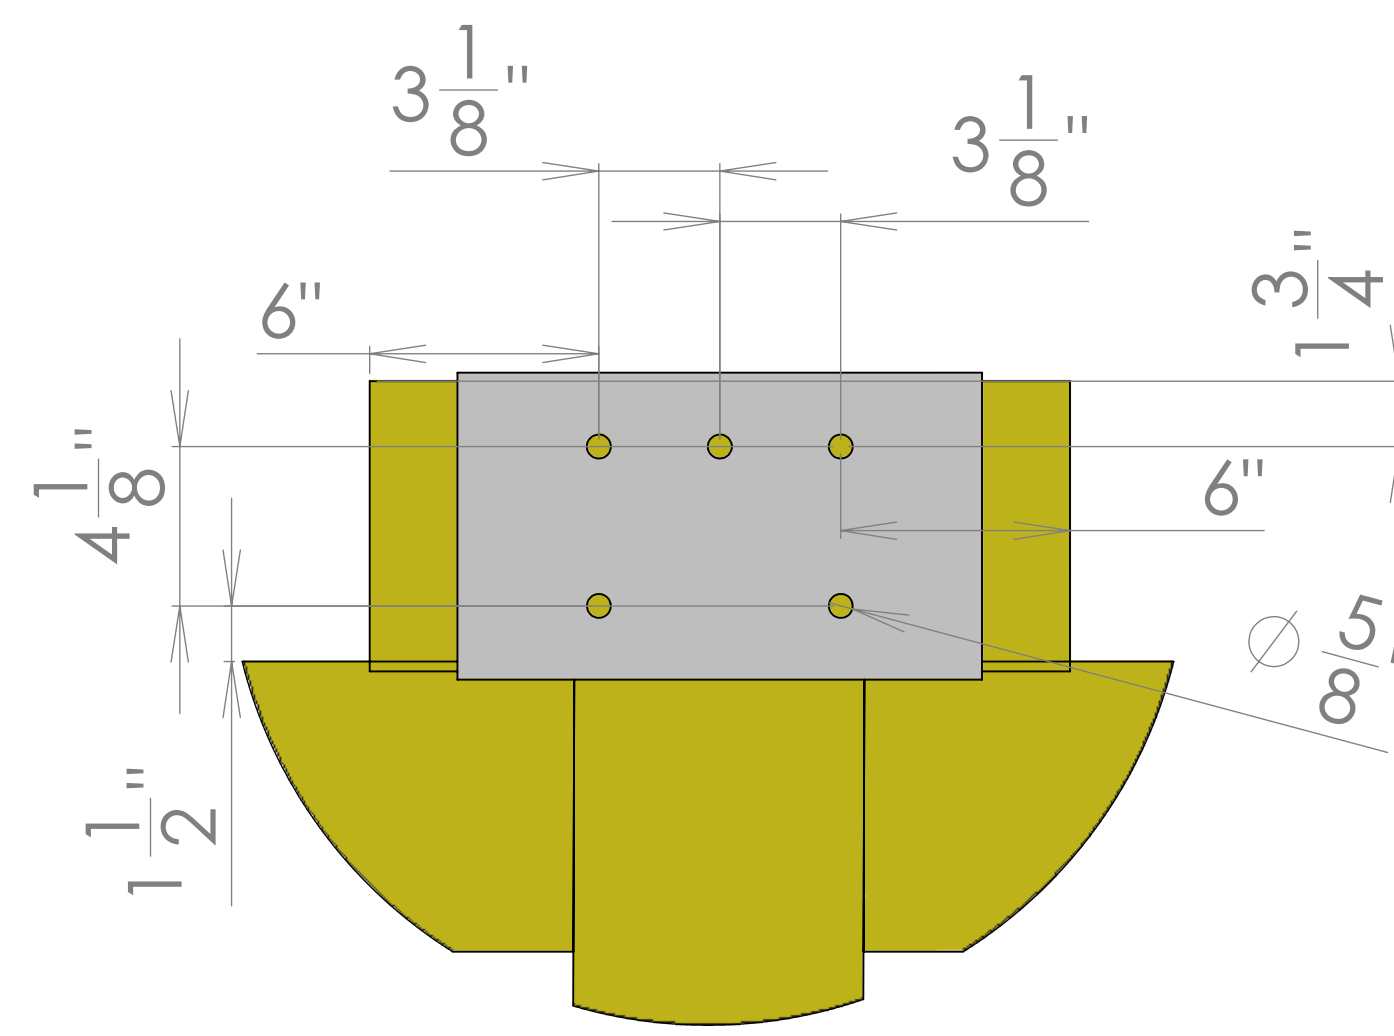

DETALLE C
ESCALA 1:5

NOTAS TÉCNICAS:
- NO UTILIZAR LAS MEDIDAS PLASMADAS EN LA PARTE SUPERIOR IZQUIERDA PARA CORTAR LAS VIGAS O CHANNEL.
- ESTE ES EL PASO 2 DEL 1ER PREFABRICADO.
- SI SOBРАН CHANNEL UTILIZARLO PARA LA PARTE DEL WINCH PARA REFORZAR LA ESTRUCTURA.
- EN ESTE PLANO ESTAN LOS AGUJEROS QUE LLEVA EL MARCO REALIZADO EN EL PLANO #1 EN LA PARTE SUPERIOR. TAMBIEN TIENE LAS MEDIDAS DEL CORTE DE LAS VIGAS Y LOS CHANNEL.

DIBUJANTE:		NELSON JUNIOR RAMIREZ	
NOMBRE DE PROYECTO:		ROMANA(CUBILOTE)	
EMPRESA:		APROBADO POR:	
		FECHA: 14/10/2025	
		MEDIDAS EN PULGADAS	