

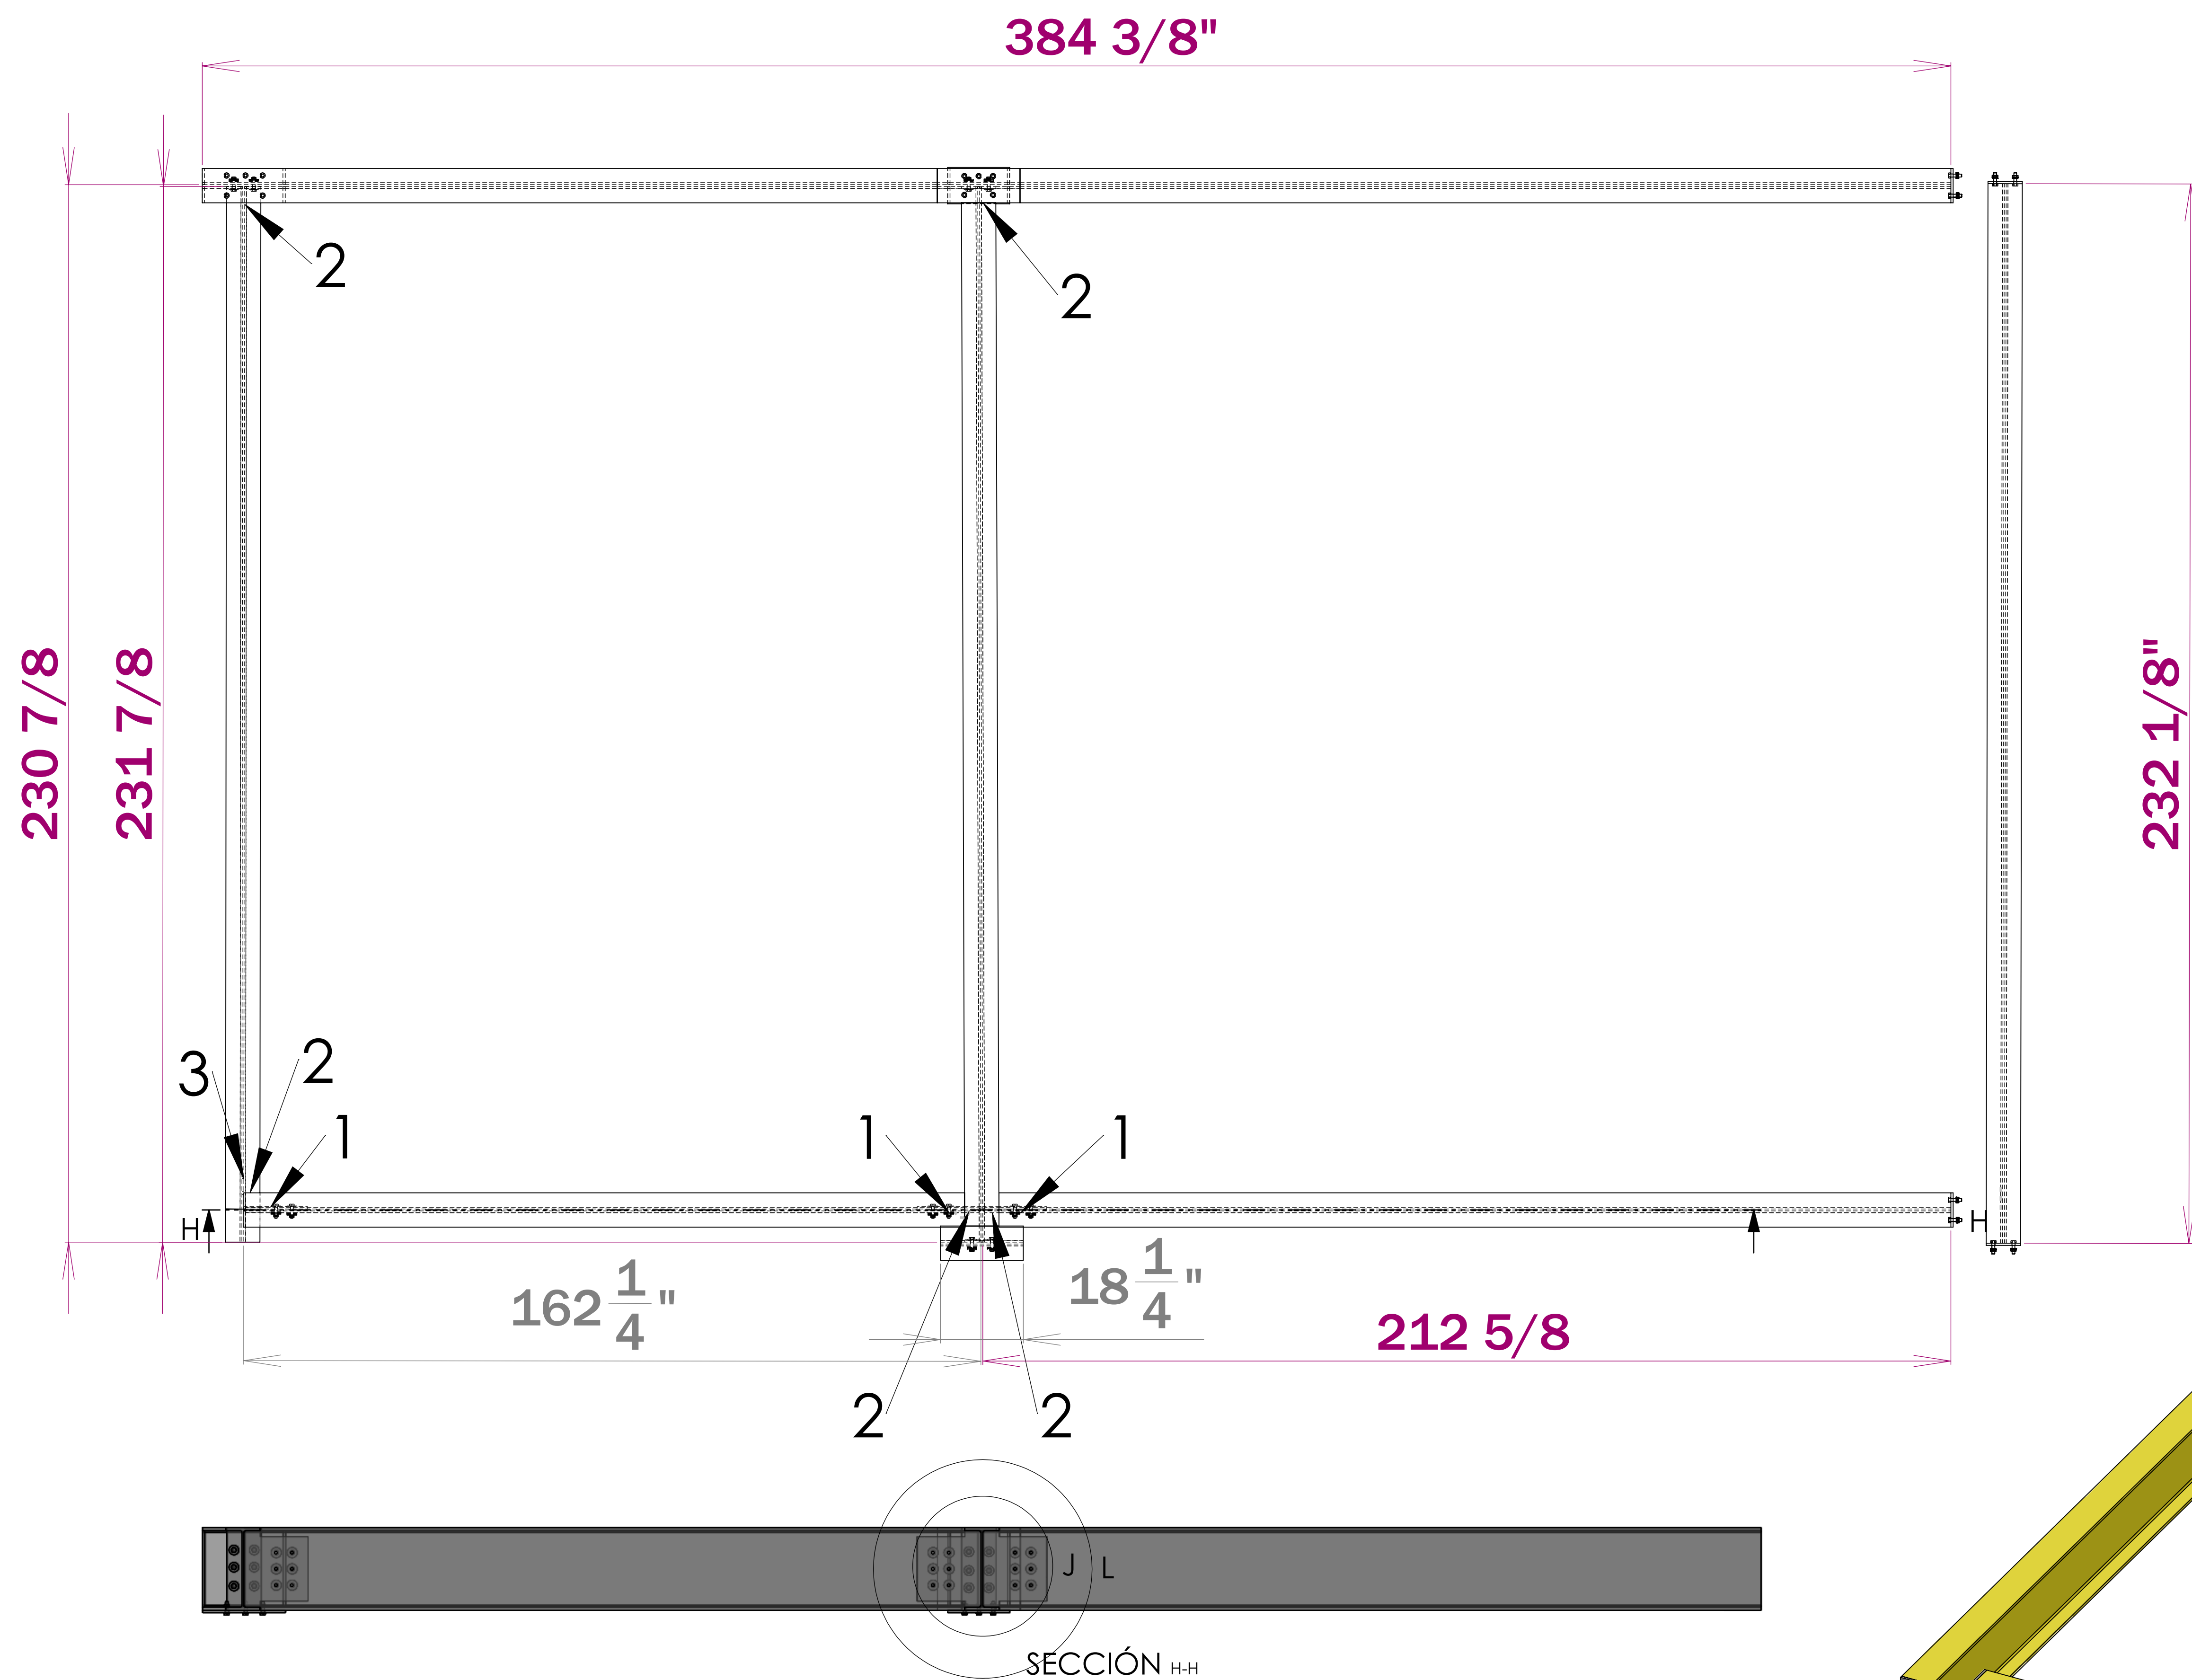
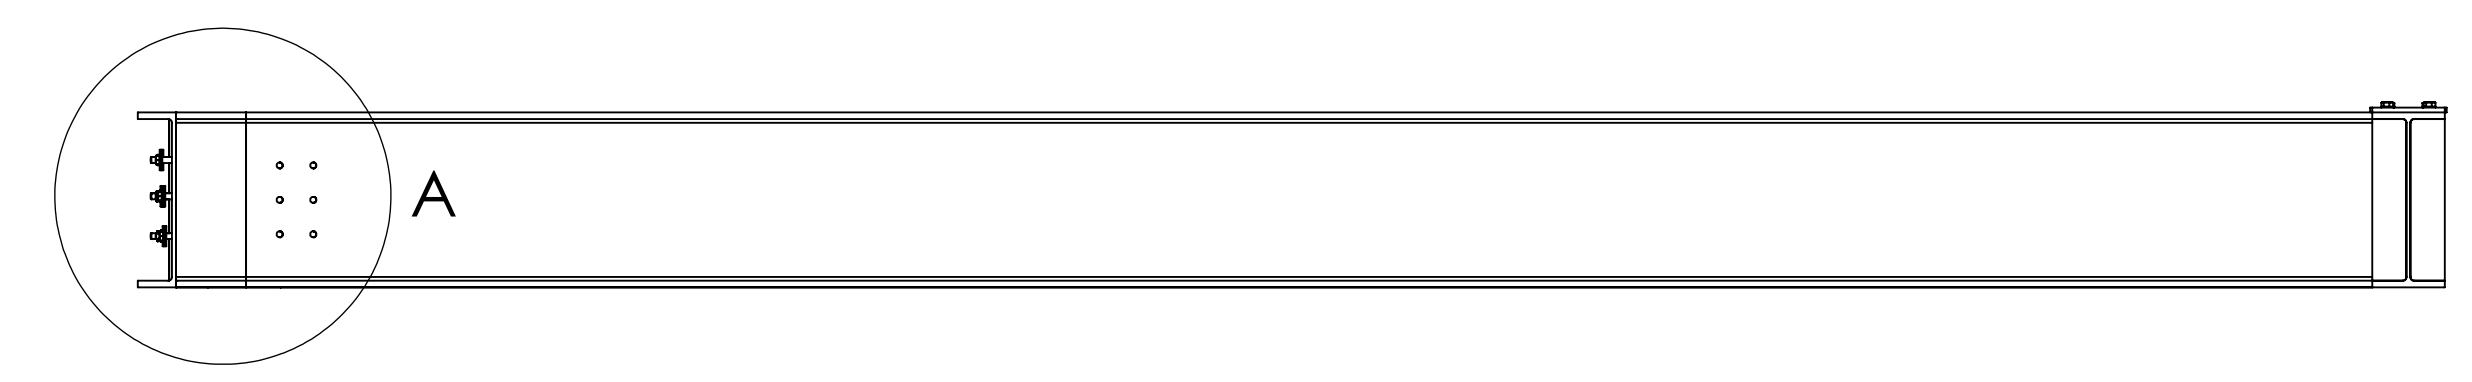
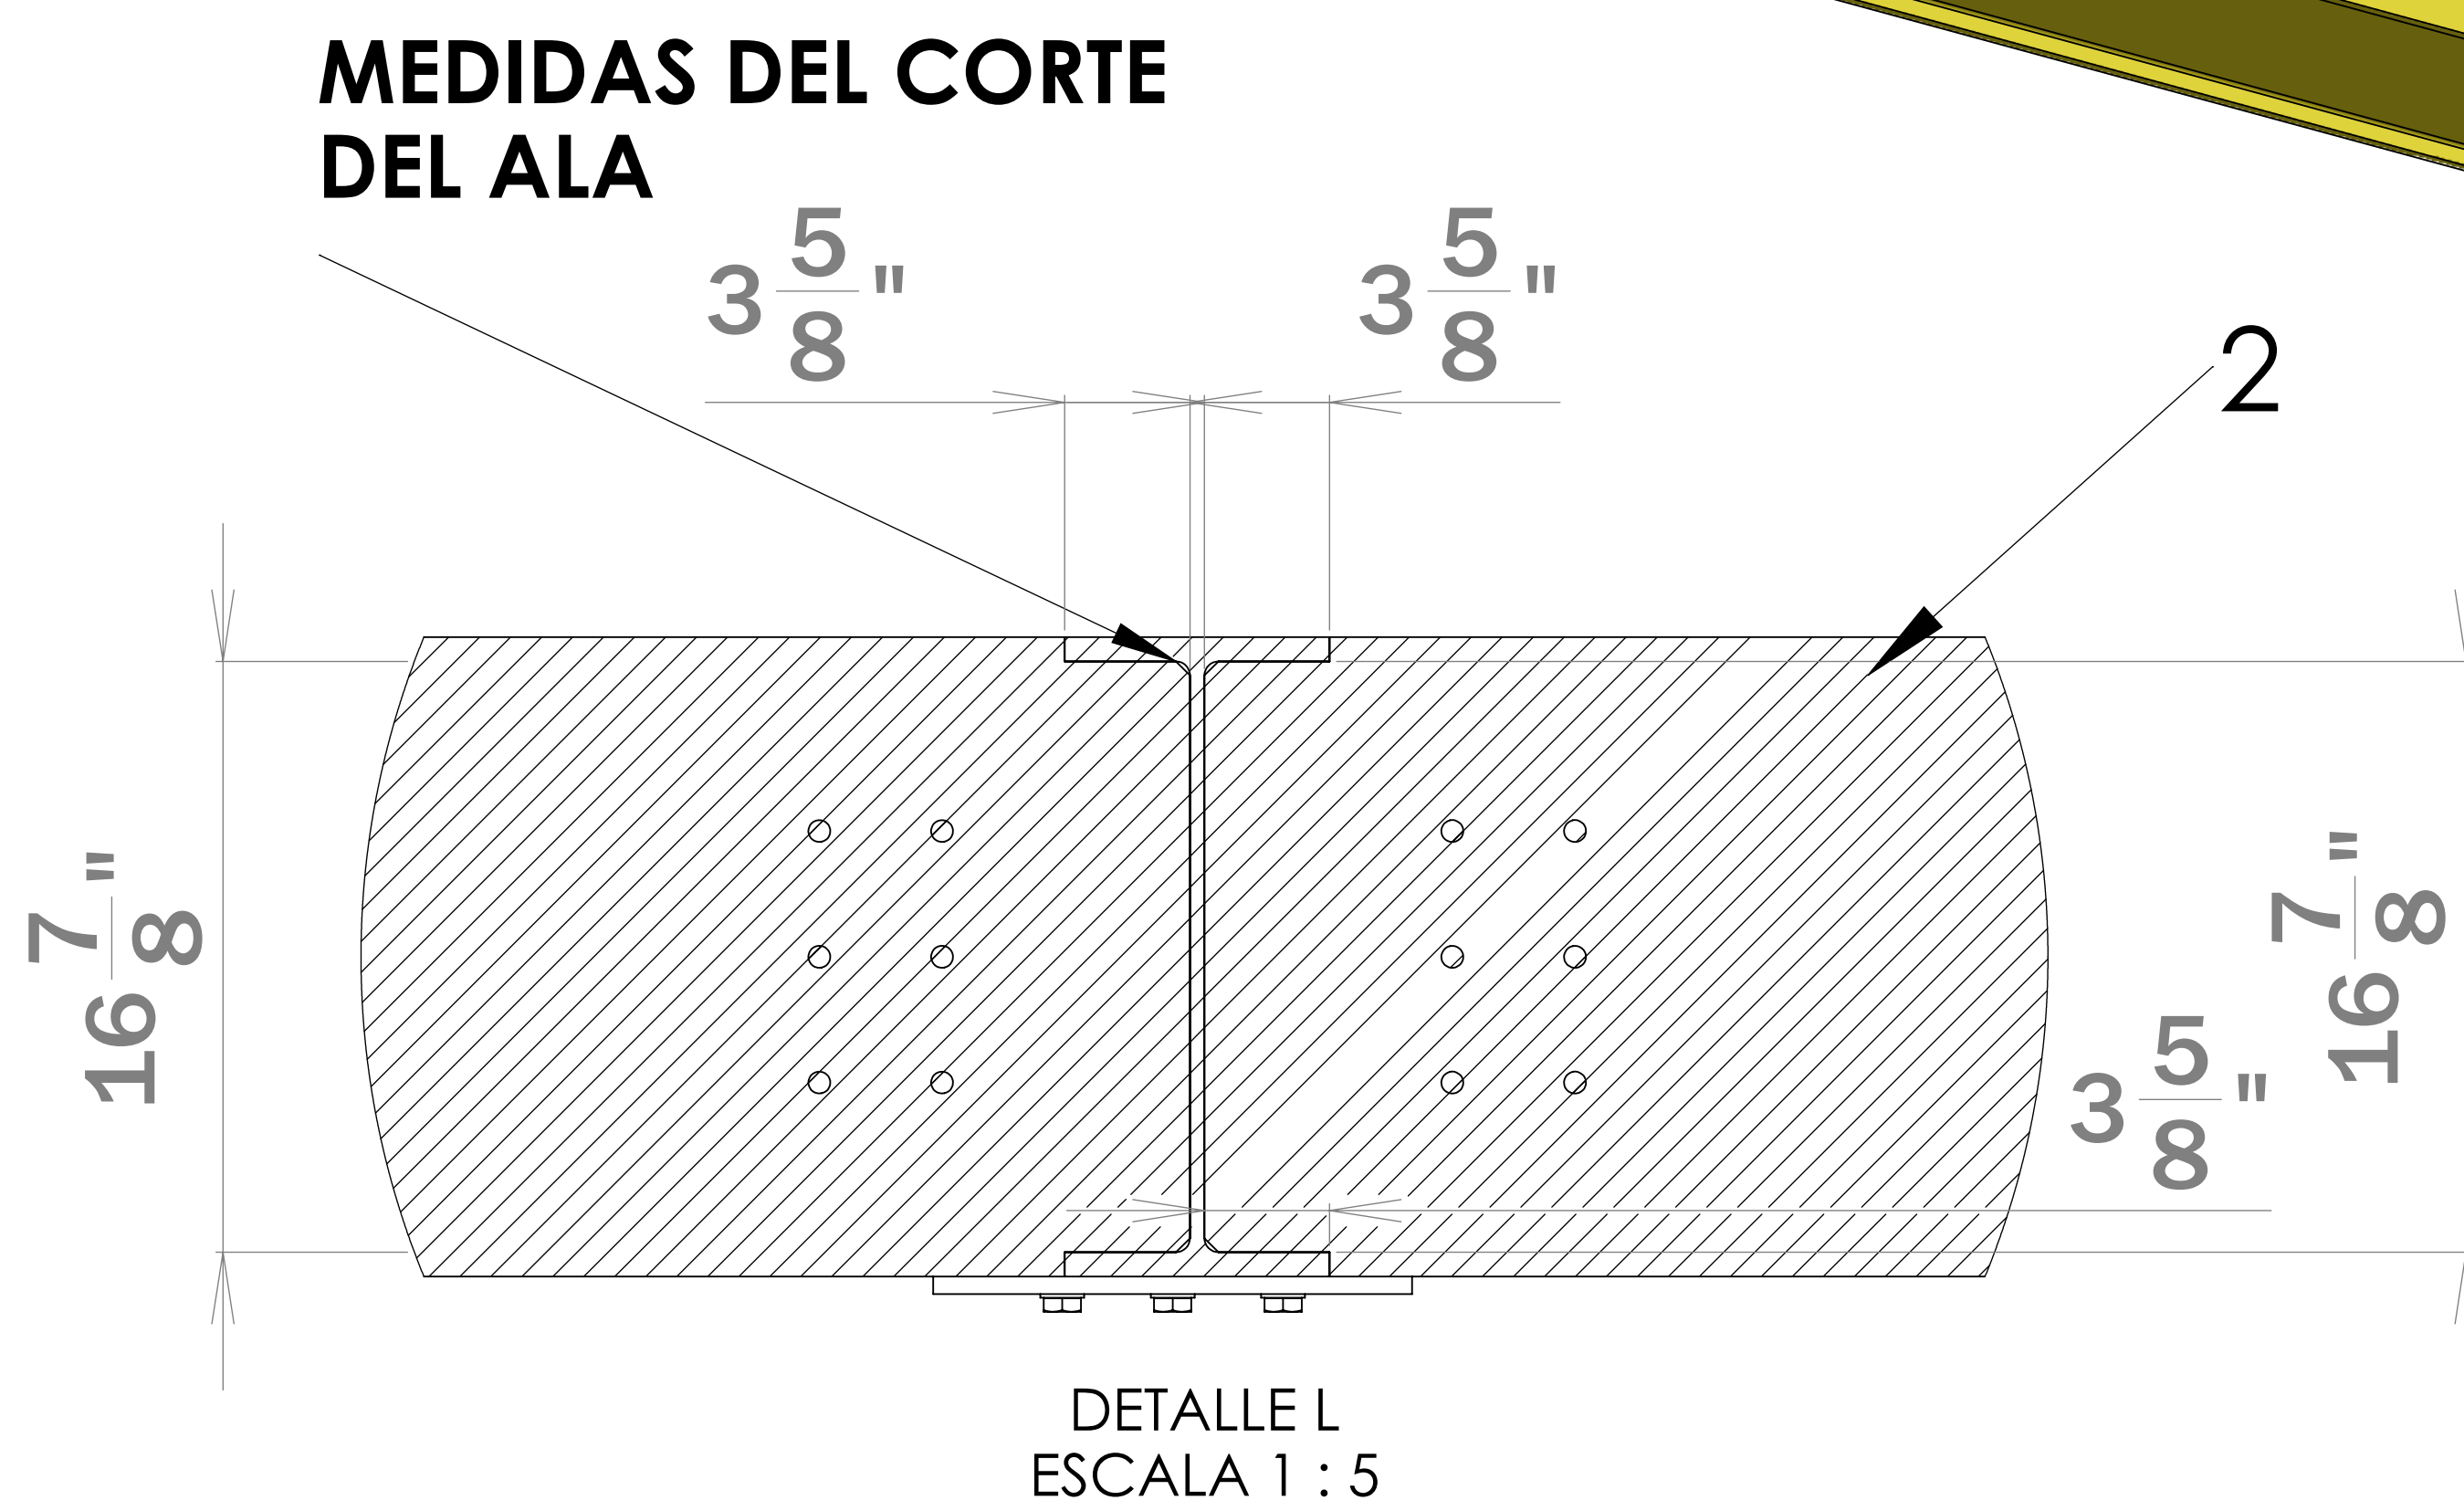
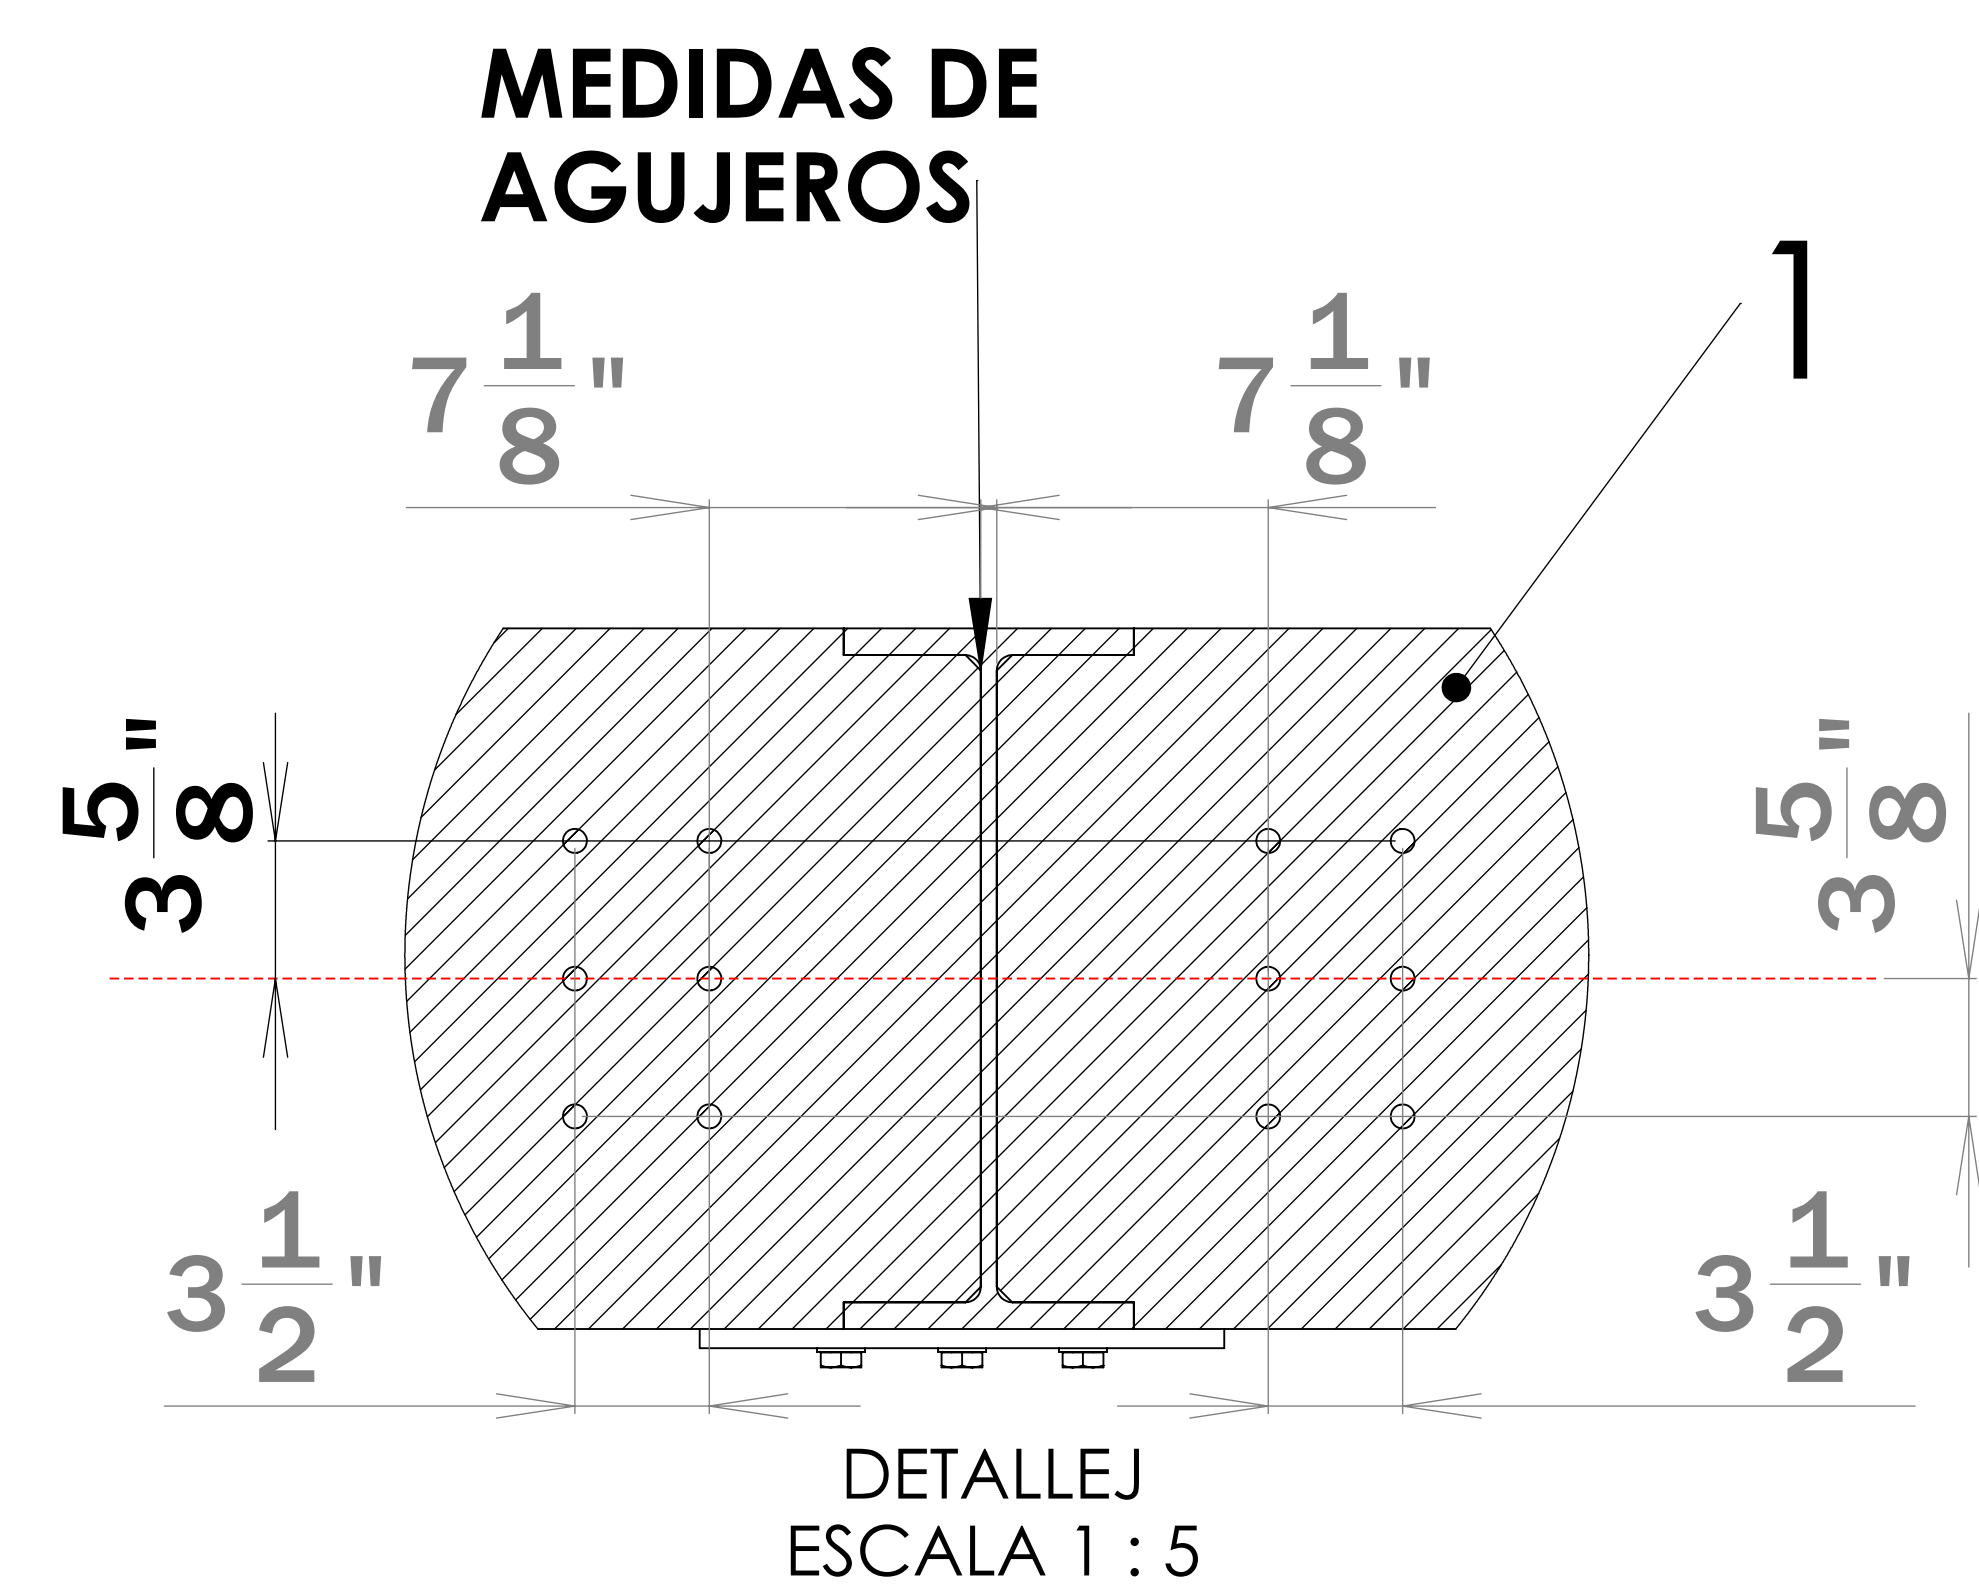


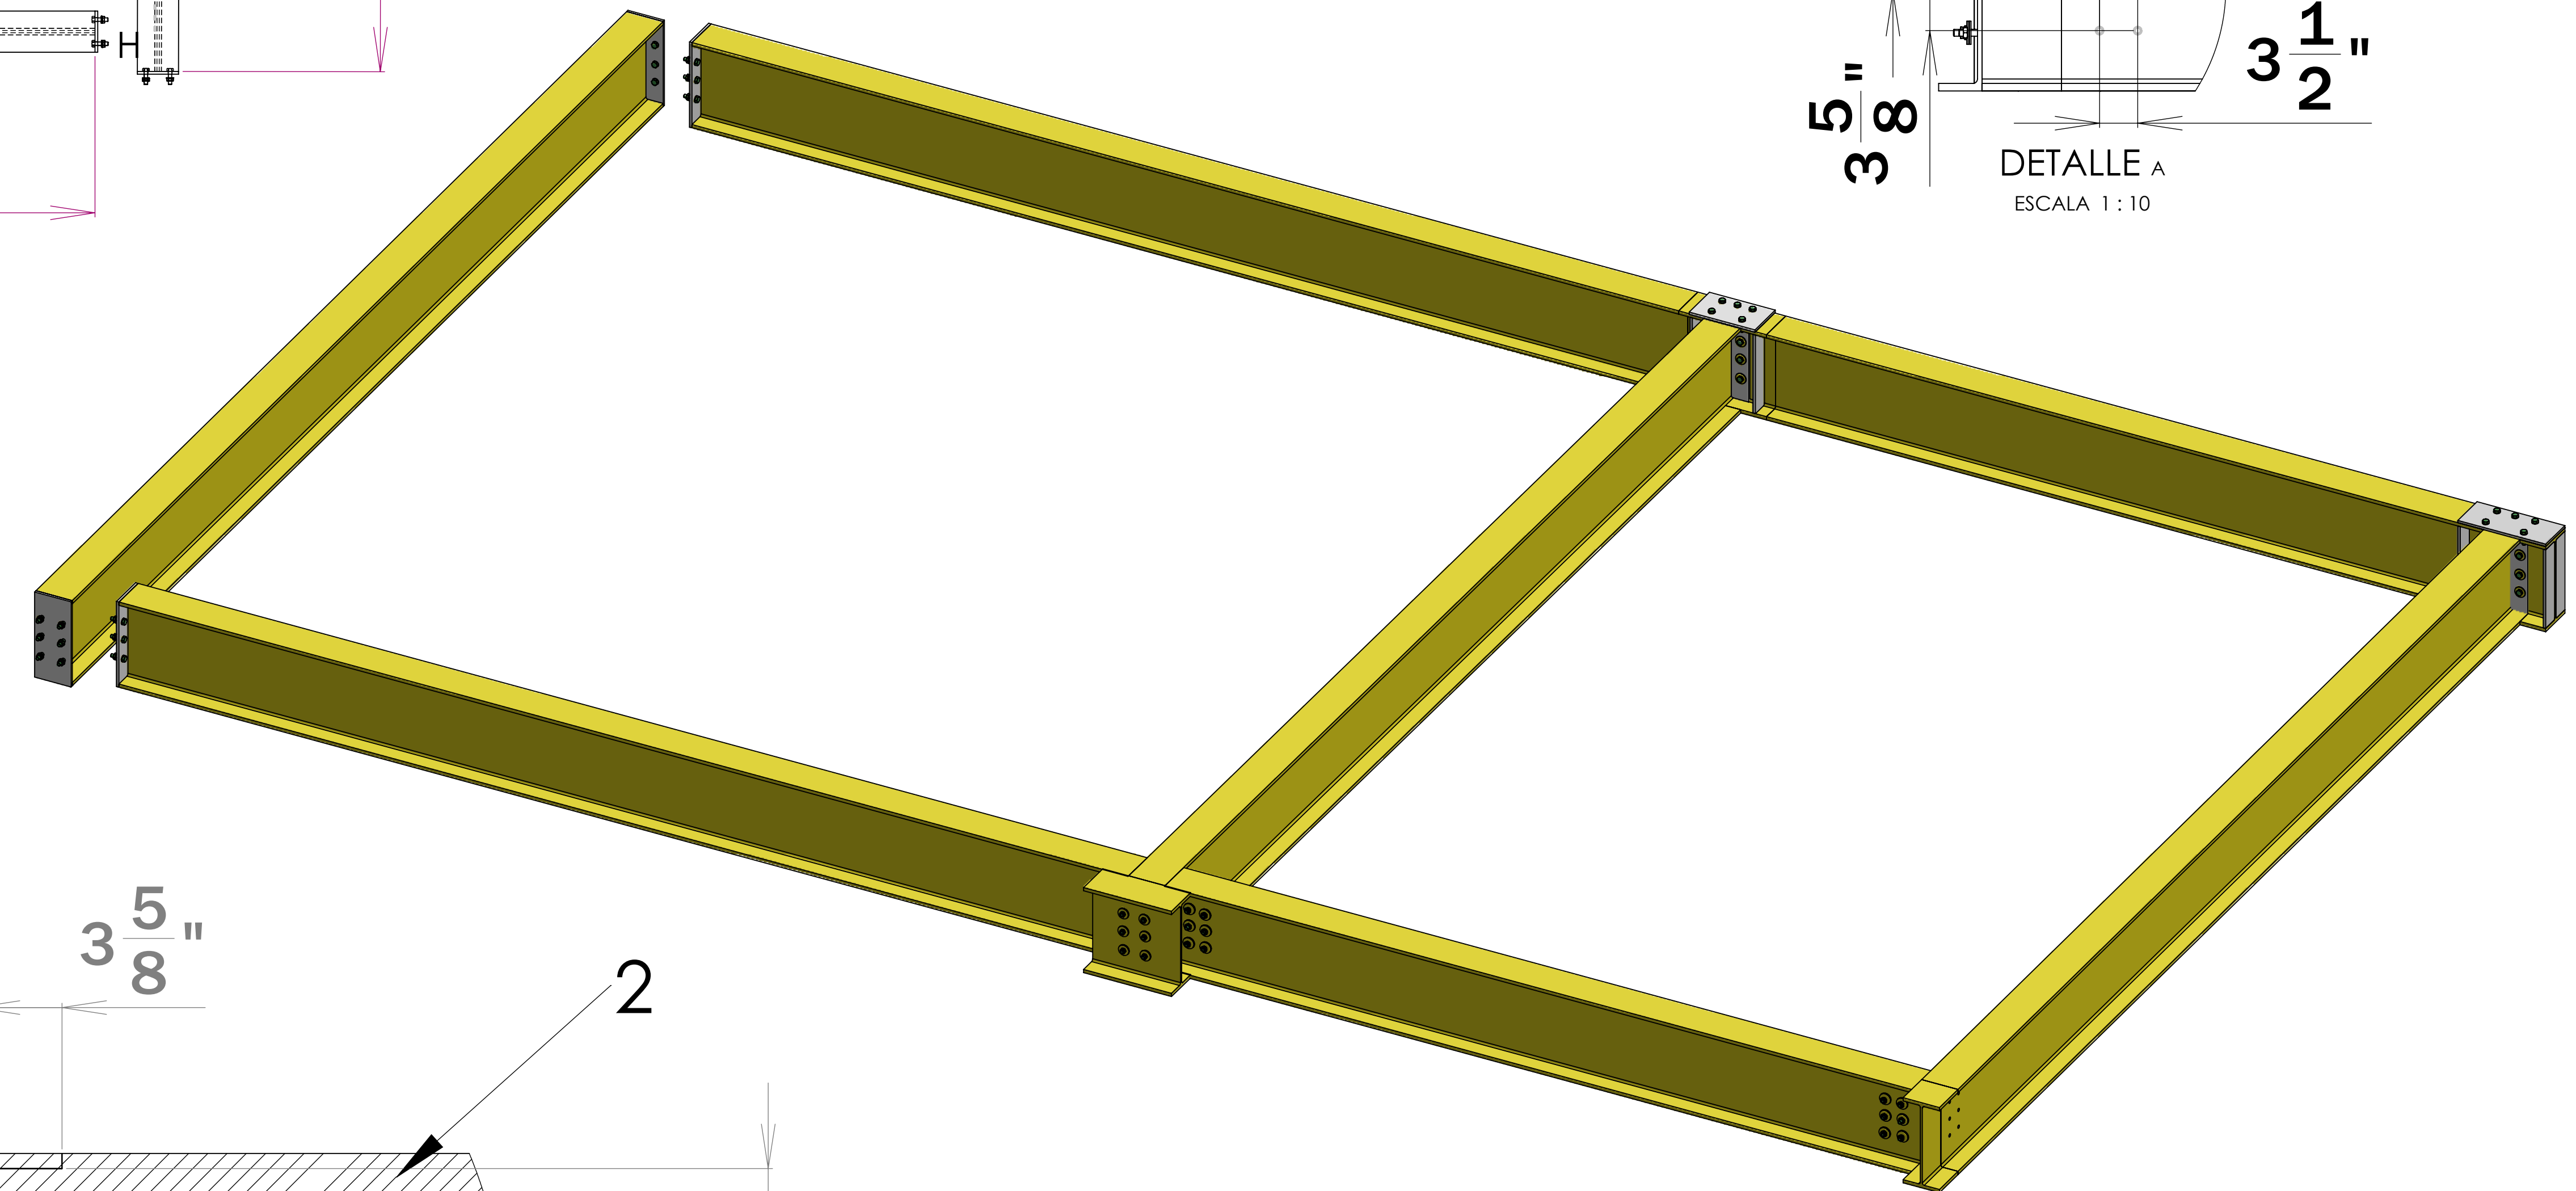

- NOTAS TECNICAS:**
- ESTE ES EL PRIMER PASO DEL PREFABRICADO DE LA ETAPA #1
 - TENER MUY PENDIENTE QUE LAS MEDIDAS ESTAN EN PULGADAS
 - LAS MEDIDAS DE LOS AGUJEROS ESTAN EN EL DETALLE J Y LAS DEL CORTE DE LA VIGA EN EL DETALLE L
 - ES EL MISMO CORTE DE ALA PARA TODAS LAS VIGAS DE ESTE PLANO.
 - LOS AGUJEROS SON 5/8
 - EL #1 SIGNIFICA, QUE ESA PARTE UTILIZARA LAS MEDIDAS DEL DETALLE J.
 - EL #2 SIGNIFICA: QUE ESA PARTE DEBERA CORTARSE EL ALA UTILIZANDO LAS MEDIDAS DEL DETALLE L
 - EL #3 SIGNIFICA: QUE ESA PARTE UTILIZARA LAS MEDIDAS DEL DETALLE A

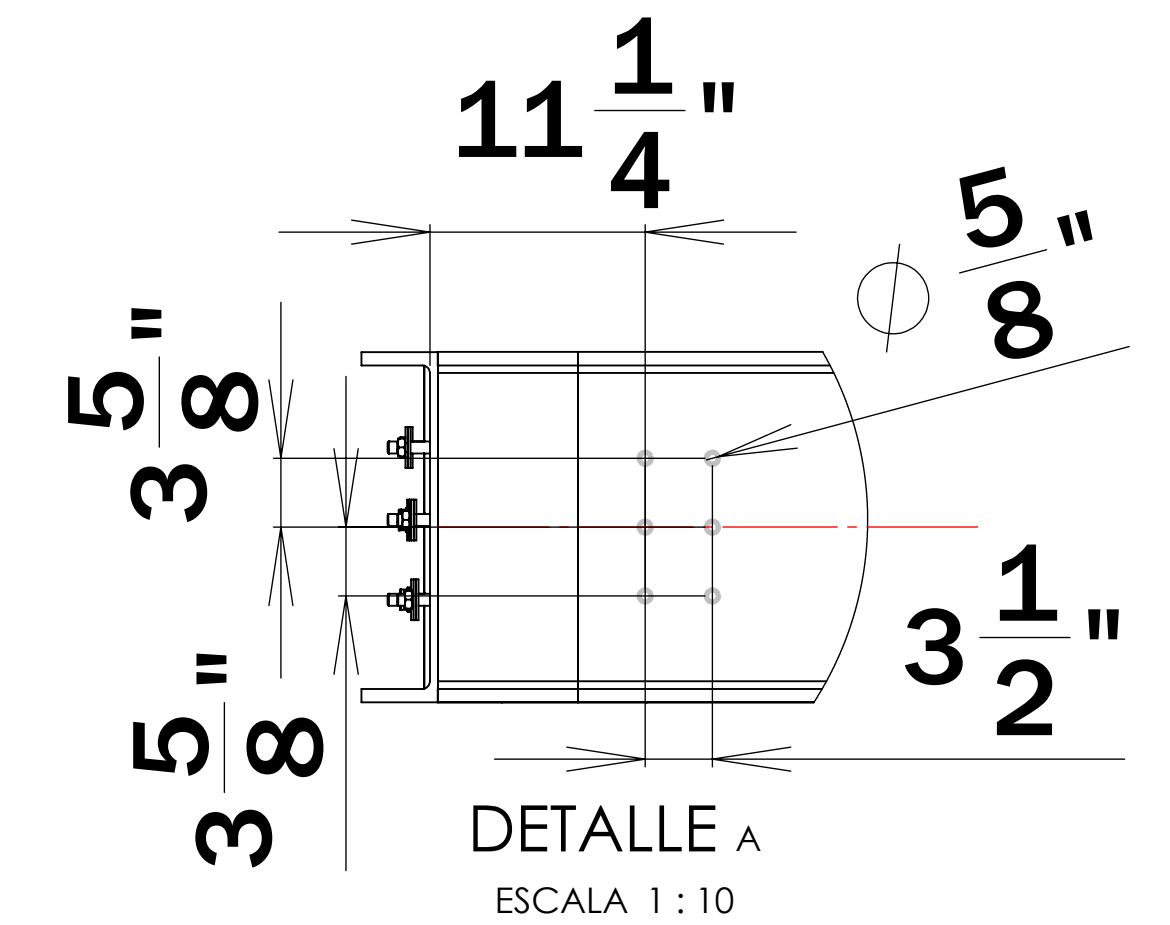

DIBUJANTE:		NELSON JUNIOR RAMIREZ	
NOMBRE DE PROYECTO: ROMANA(CUBILOTE)			
EMPRESA:		APROBADO POR:	
		FECHA: 14/10/2025	
		MEDIDAS EN PULGADAS	